


Framing Plan - Truck Dump Stilling Shed

Reference: S01, S03, & S04

1. Top of Steel Elevation 149-9 U.N.
2. All WT12x38 EL: 149-2 W/Stem Oriented Up.
3. L4x3 1/2x5 1/16 Bracing EL: 149-7


0	For Field Use	May 22 2025	KR
A	For Approval	Apr 2 2025	CR
REV	DATE BY		
DESCRIPTION			
FABRICATOR	DETAILER	DATE	BY
	Nxt Gen Steel Detailing, LLC	DRAWN:	(02-12-25) CR
PEPPER TANK & CONTRACTING	881 W. Yellowstone Hwy, Casper WY 82602 • (307) 234-3533 • www.peppertank.com	CHKD:	05 22 25 NG
		HOLES:	13/16" UNO
JOB NAME:	NARM - Stilling Shed Truck Dump (Circuit One)	BOLTS:	3/8" A325N UNO
LOCATION:	North Antelope Rochelle Mine - Gillette, WY.	WELDS:	E70XX
CONTRACTOR:	Hladky Construction	CLEAN:	
SHEET DESCRIPTION:	JOB NUMBER:	SHEET NUMBER:	REV#
Framing Plan @ Elevation 129-9 U.N.	24-36N	E4	0

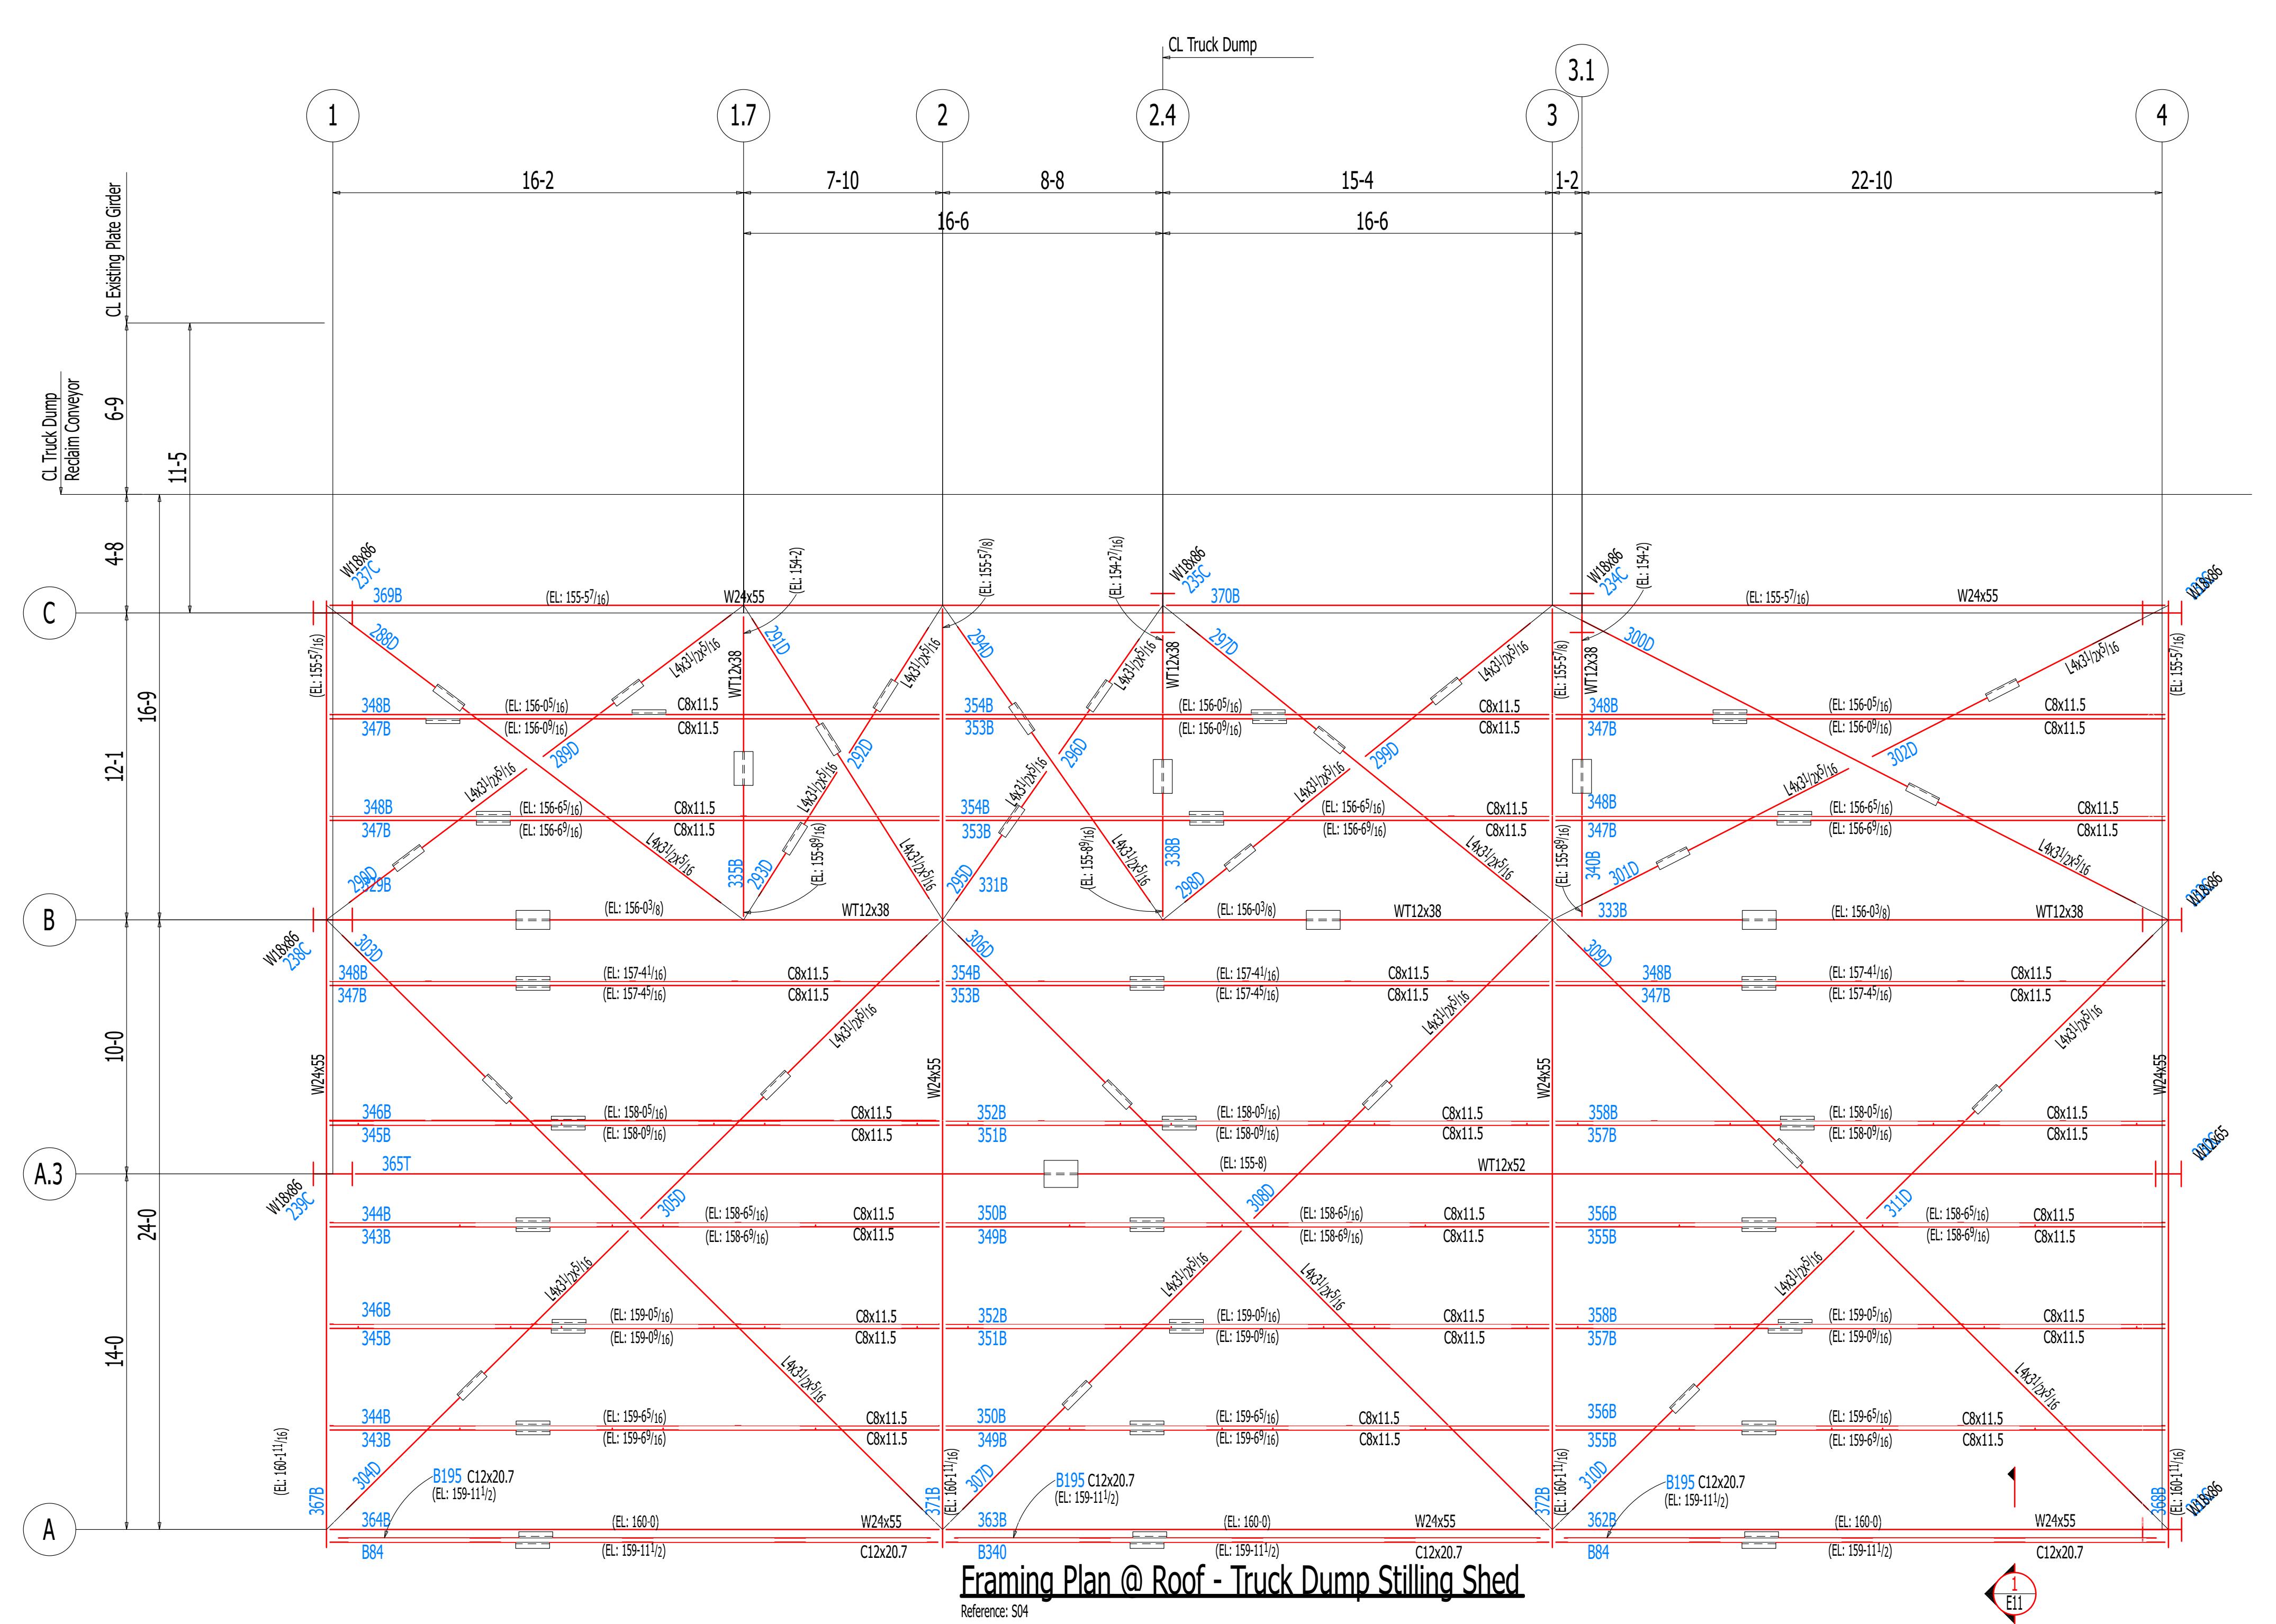


Framing Plan @ Roof - T

Training Plan @ RDU - Truck


Reference: S04

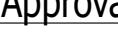0	For Field Use		May 22 2025	KR	
A	For Approval		Apr 2 2025	CR	
REV	DESCRIPTION		DATE	BY	
FABRICATOR	DETAILER		DATE	BY	
 PEPPER TANK & CONTRACTING 801 W. Yellowstone Hwy, Casper WY 82602 - (307) 234-3533 - www.peppertank.com	 Nxt Gen Steel Detailing, LLC <i>Structural & Miscellaneous</i> PO Box 846 Basin, Wyoming 82410 307-272-5418 or 307-272-7031		DRAWN:	02-12-25	CR
			CHKD:	05 22 25	NG
			HOLES:	13/16Ø UNO	
JOB NAME:	NARM - Stilling Shed Truck Dump (Circuit One)		BOLTS:	3/4Ø A325N UNO	
LOCATION:	North Antelope Rochelle Mine - Gillette, Wy.		WELDS:	E70XX	
CONTRACTOR:	Hladky Construction		CLEAN:		
SHEET DESCRIPTION:			PAINT:		
Framing Plan & Roof		JOB NUMBER:	24-36N	SHEET NUMBER:	E5
		REV#	0		

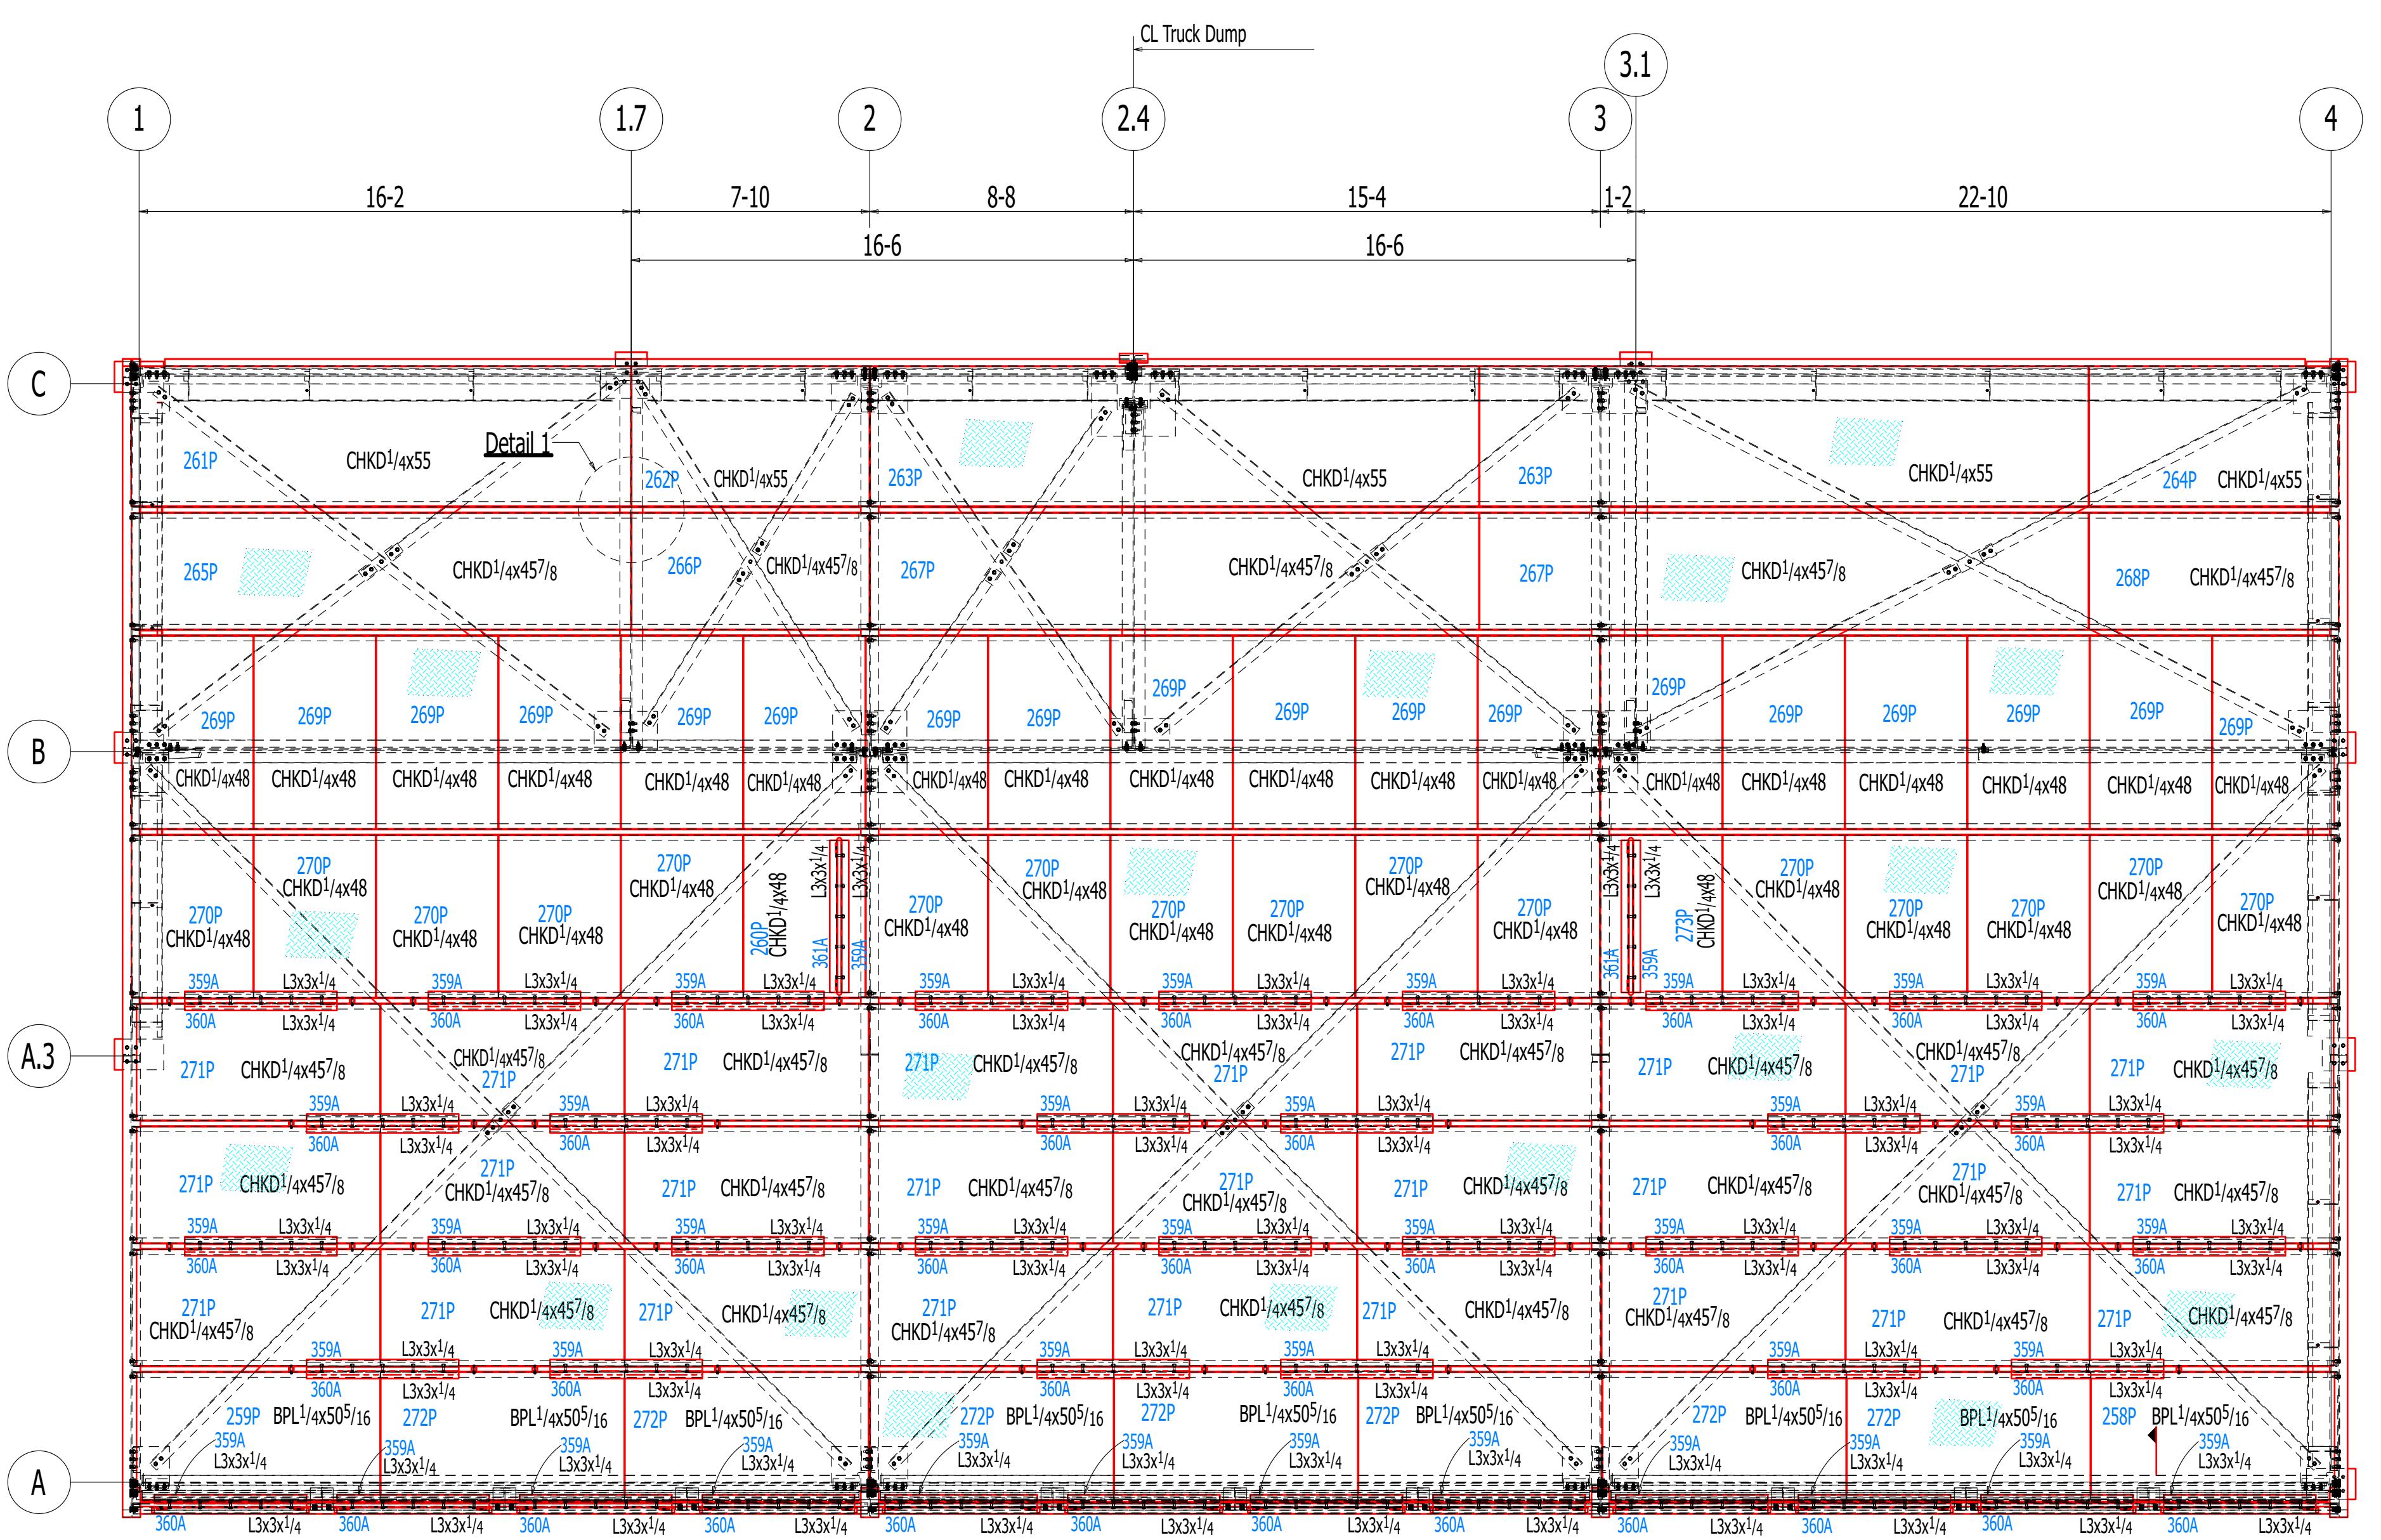
Roof PL Framing Plan - Truck Dump Stilling Shed

Reference: SOS

1. Top of Steel Elevation Varies See Plan.
2. All PL 1/4" Checked Plate.
3. Reference Detail 1/E11 for Typical Baffle Details

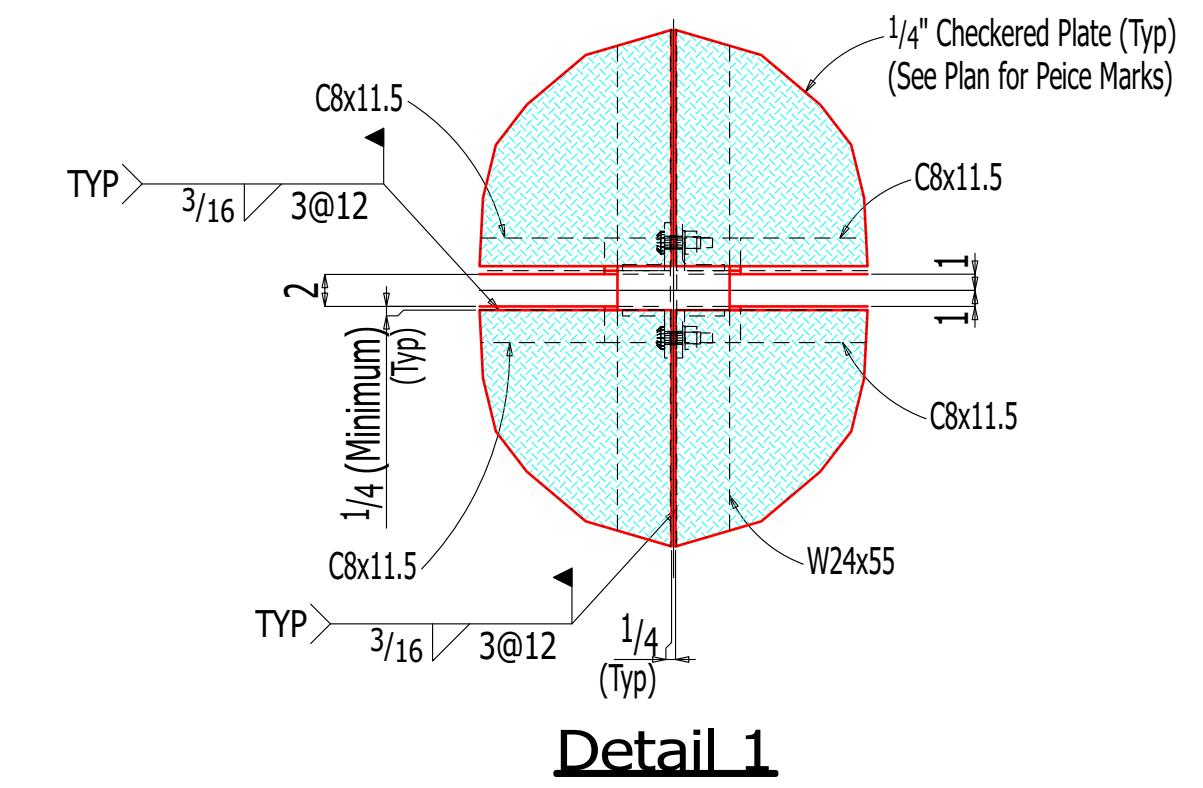
**Detail 1**


0	For Field Use	May 22 2025	KR
A	For Approval	Apr 2 2025	CR
REV	DESCRIPTION	DATE	BY
	FABRICATOR	DETAILER	DATE BY
	 Nxt Gen Steel Detailing, LLC		DRAWN: (02-12-25) CR
	PEPPER TANK & CONTRACTING		CHKD: 05 22 25 NG
			HOLES: 13/16Ø UNO
			1801 W. Yellowstone Hwy, Casper WY 82602 (307) 234-3533 www.peppertank.com
	JOB NAME: NARM - Stilling Shed Truck Dump (Circuit One)	BOLTS:	3/4" A325N UNO
	LOCATION: North Antelope Rochelle Mine - Gillette, WY.	WELDS:	E70XX
	CONTRACTOR: Hladky Construction	CLEAN:	
	SHEET DESCRIPTION: Roof PL Framing Plan	JOB NUMBER: 24-36N	REVISION: 0
		SHEET NUMBER: E6	PLOT DATE: May 22 2025

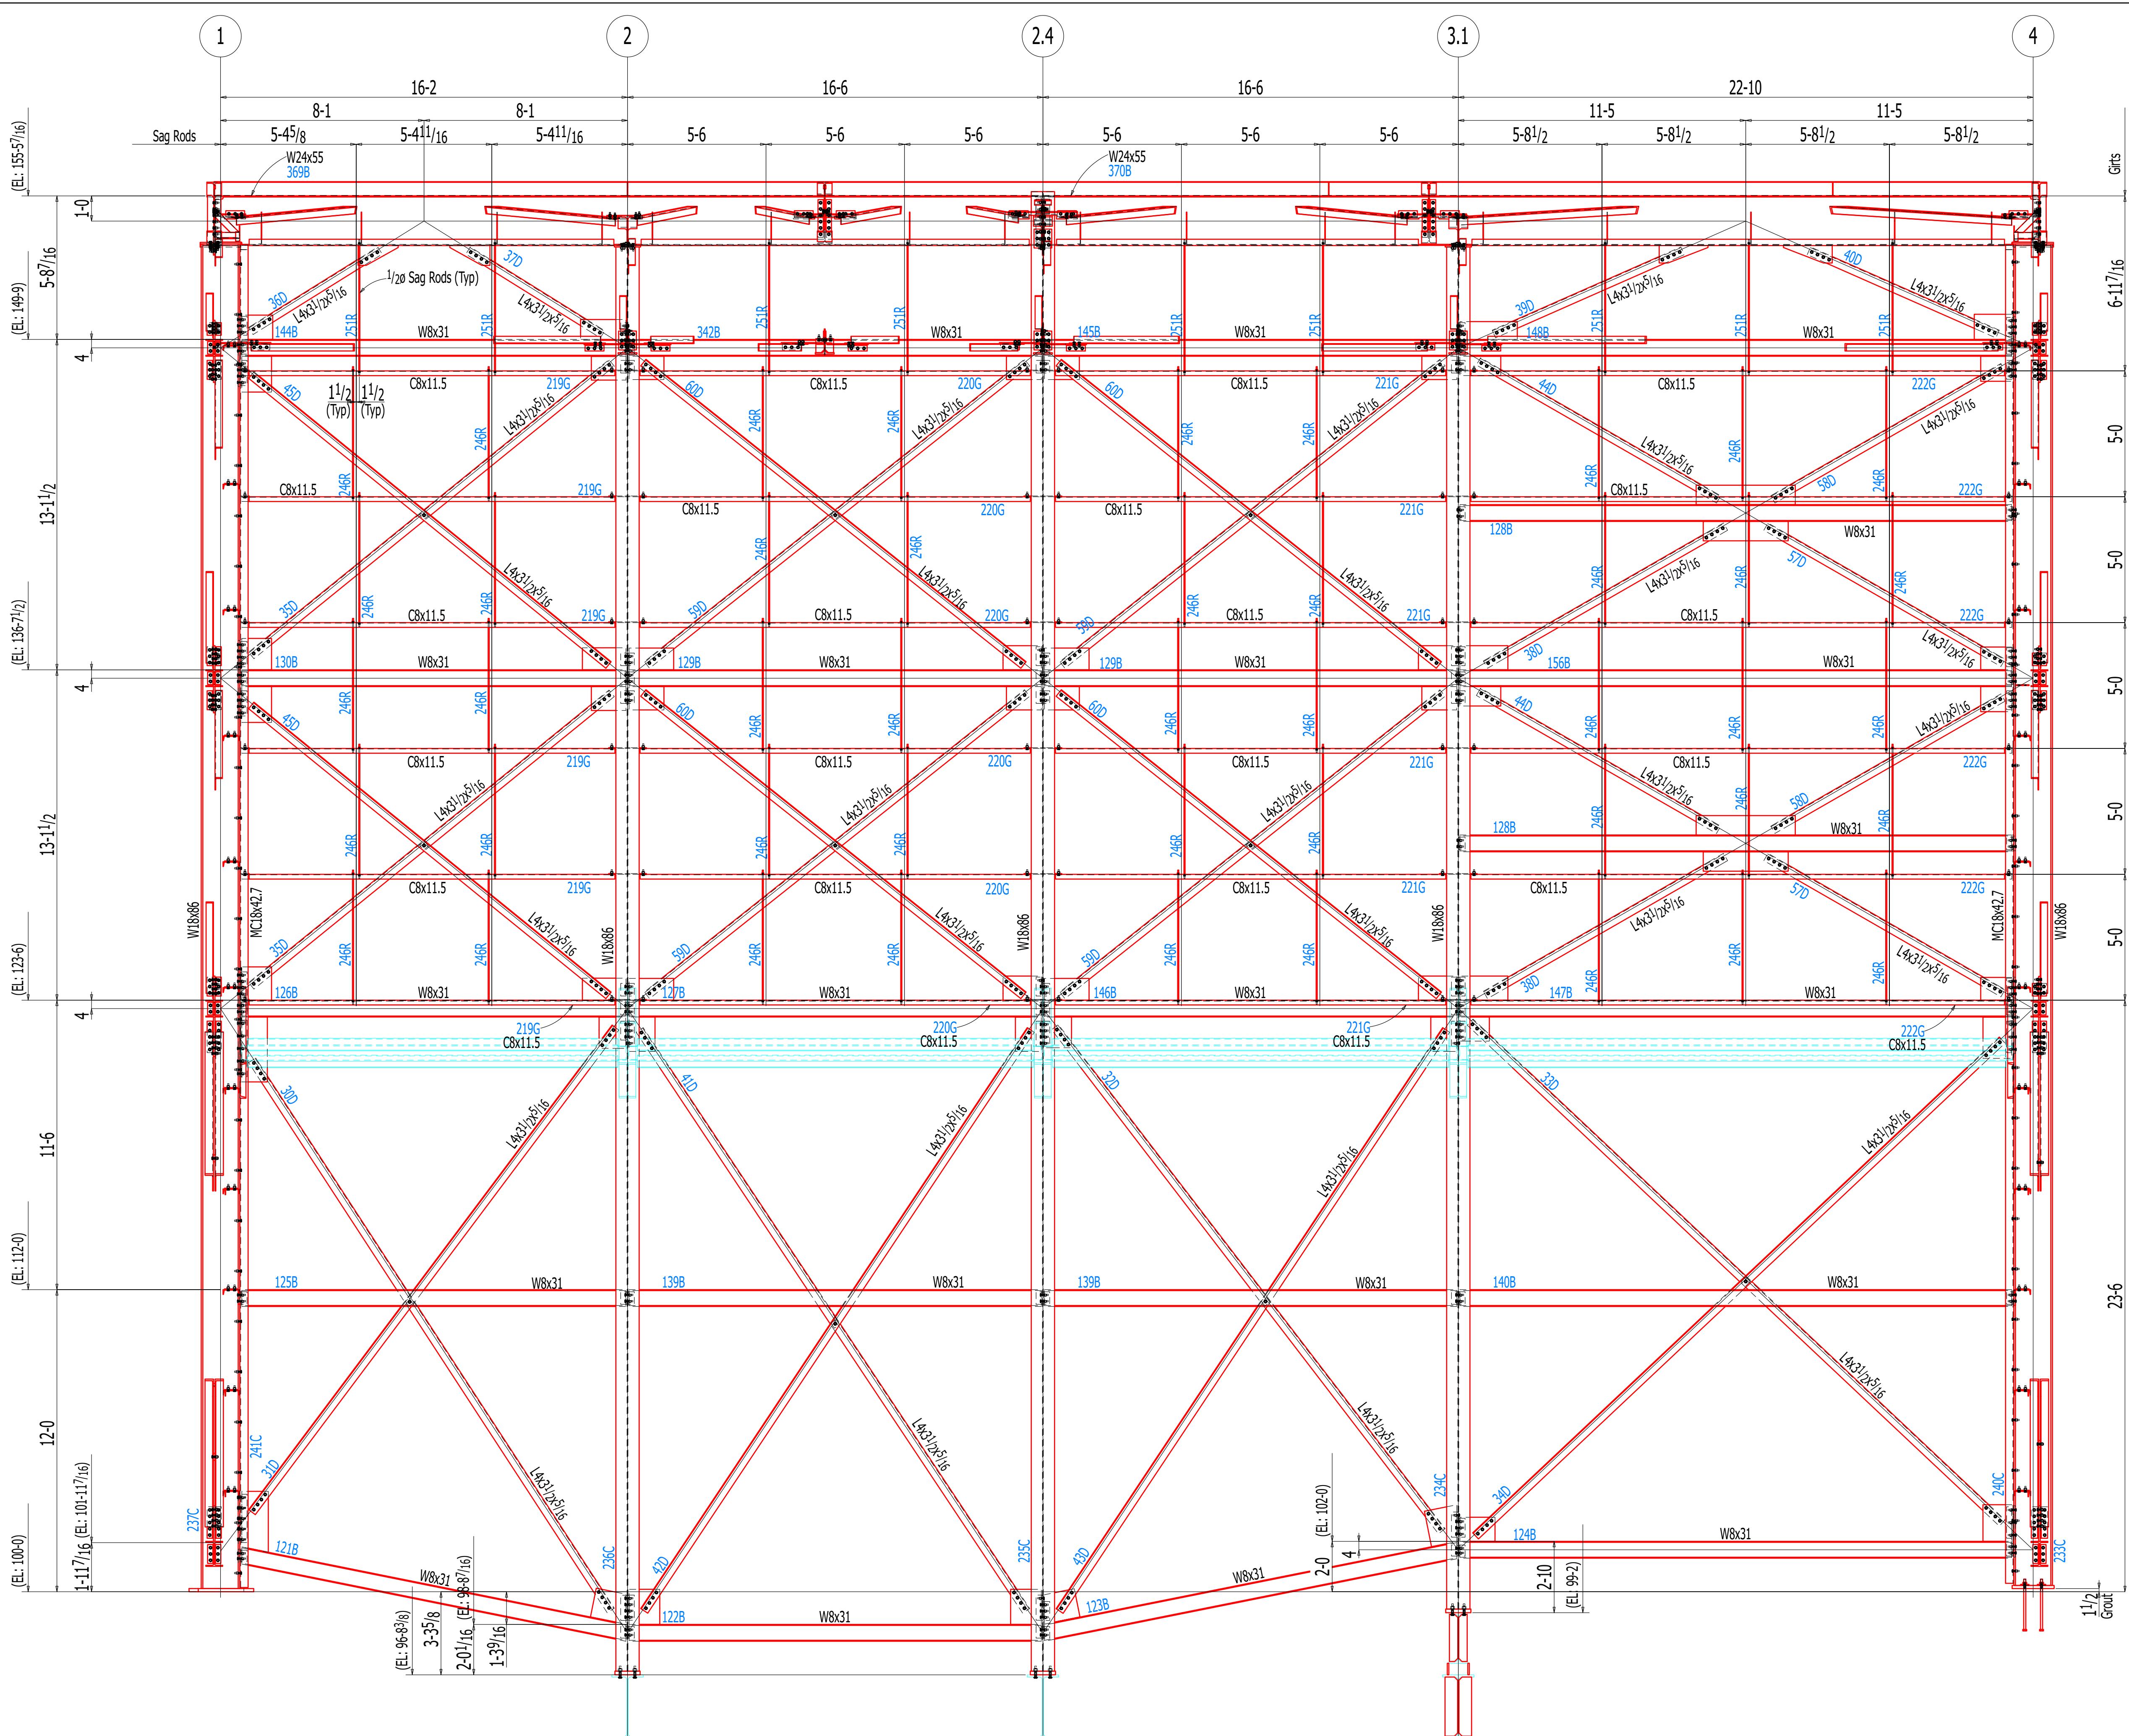

Elevation of Line C

Reference: S04
Looking East
All L4x3 1/2x5 1/16 LLV

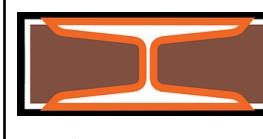0	For Field Use	May 22 2025	KR
A	For Approval	Feb 28 2025	CR
REV	DATE BY		
DESCRIPTION			
FABRICATOR	DETAILER	DATE	BY
 PEPPER TANK & CONTRACTING	 Nxt Gen Steel Detailing, LLC	DRAWN:	02-12-25 CR
1801 W. Yellowstone Hwy, Casper WY 82602 - (307) 234-3333 - www.peppertank.com		CHKD:	05 22 25 NG
HOLES:	13/16" UNO	BOLTS:	3/4" A325N UNO
WELDS:	E70XX	CLEAN:	
CONTRACTOR:	Hladky Construction	PAINT:	
SHEET DESCRIPTION:	JOB NUMBER:	SHEET NUMBER:	REV#
Elevation of Line C	24-36N	E7	0

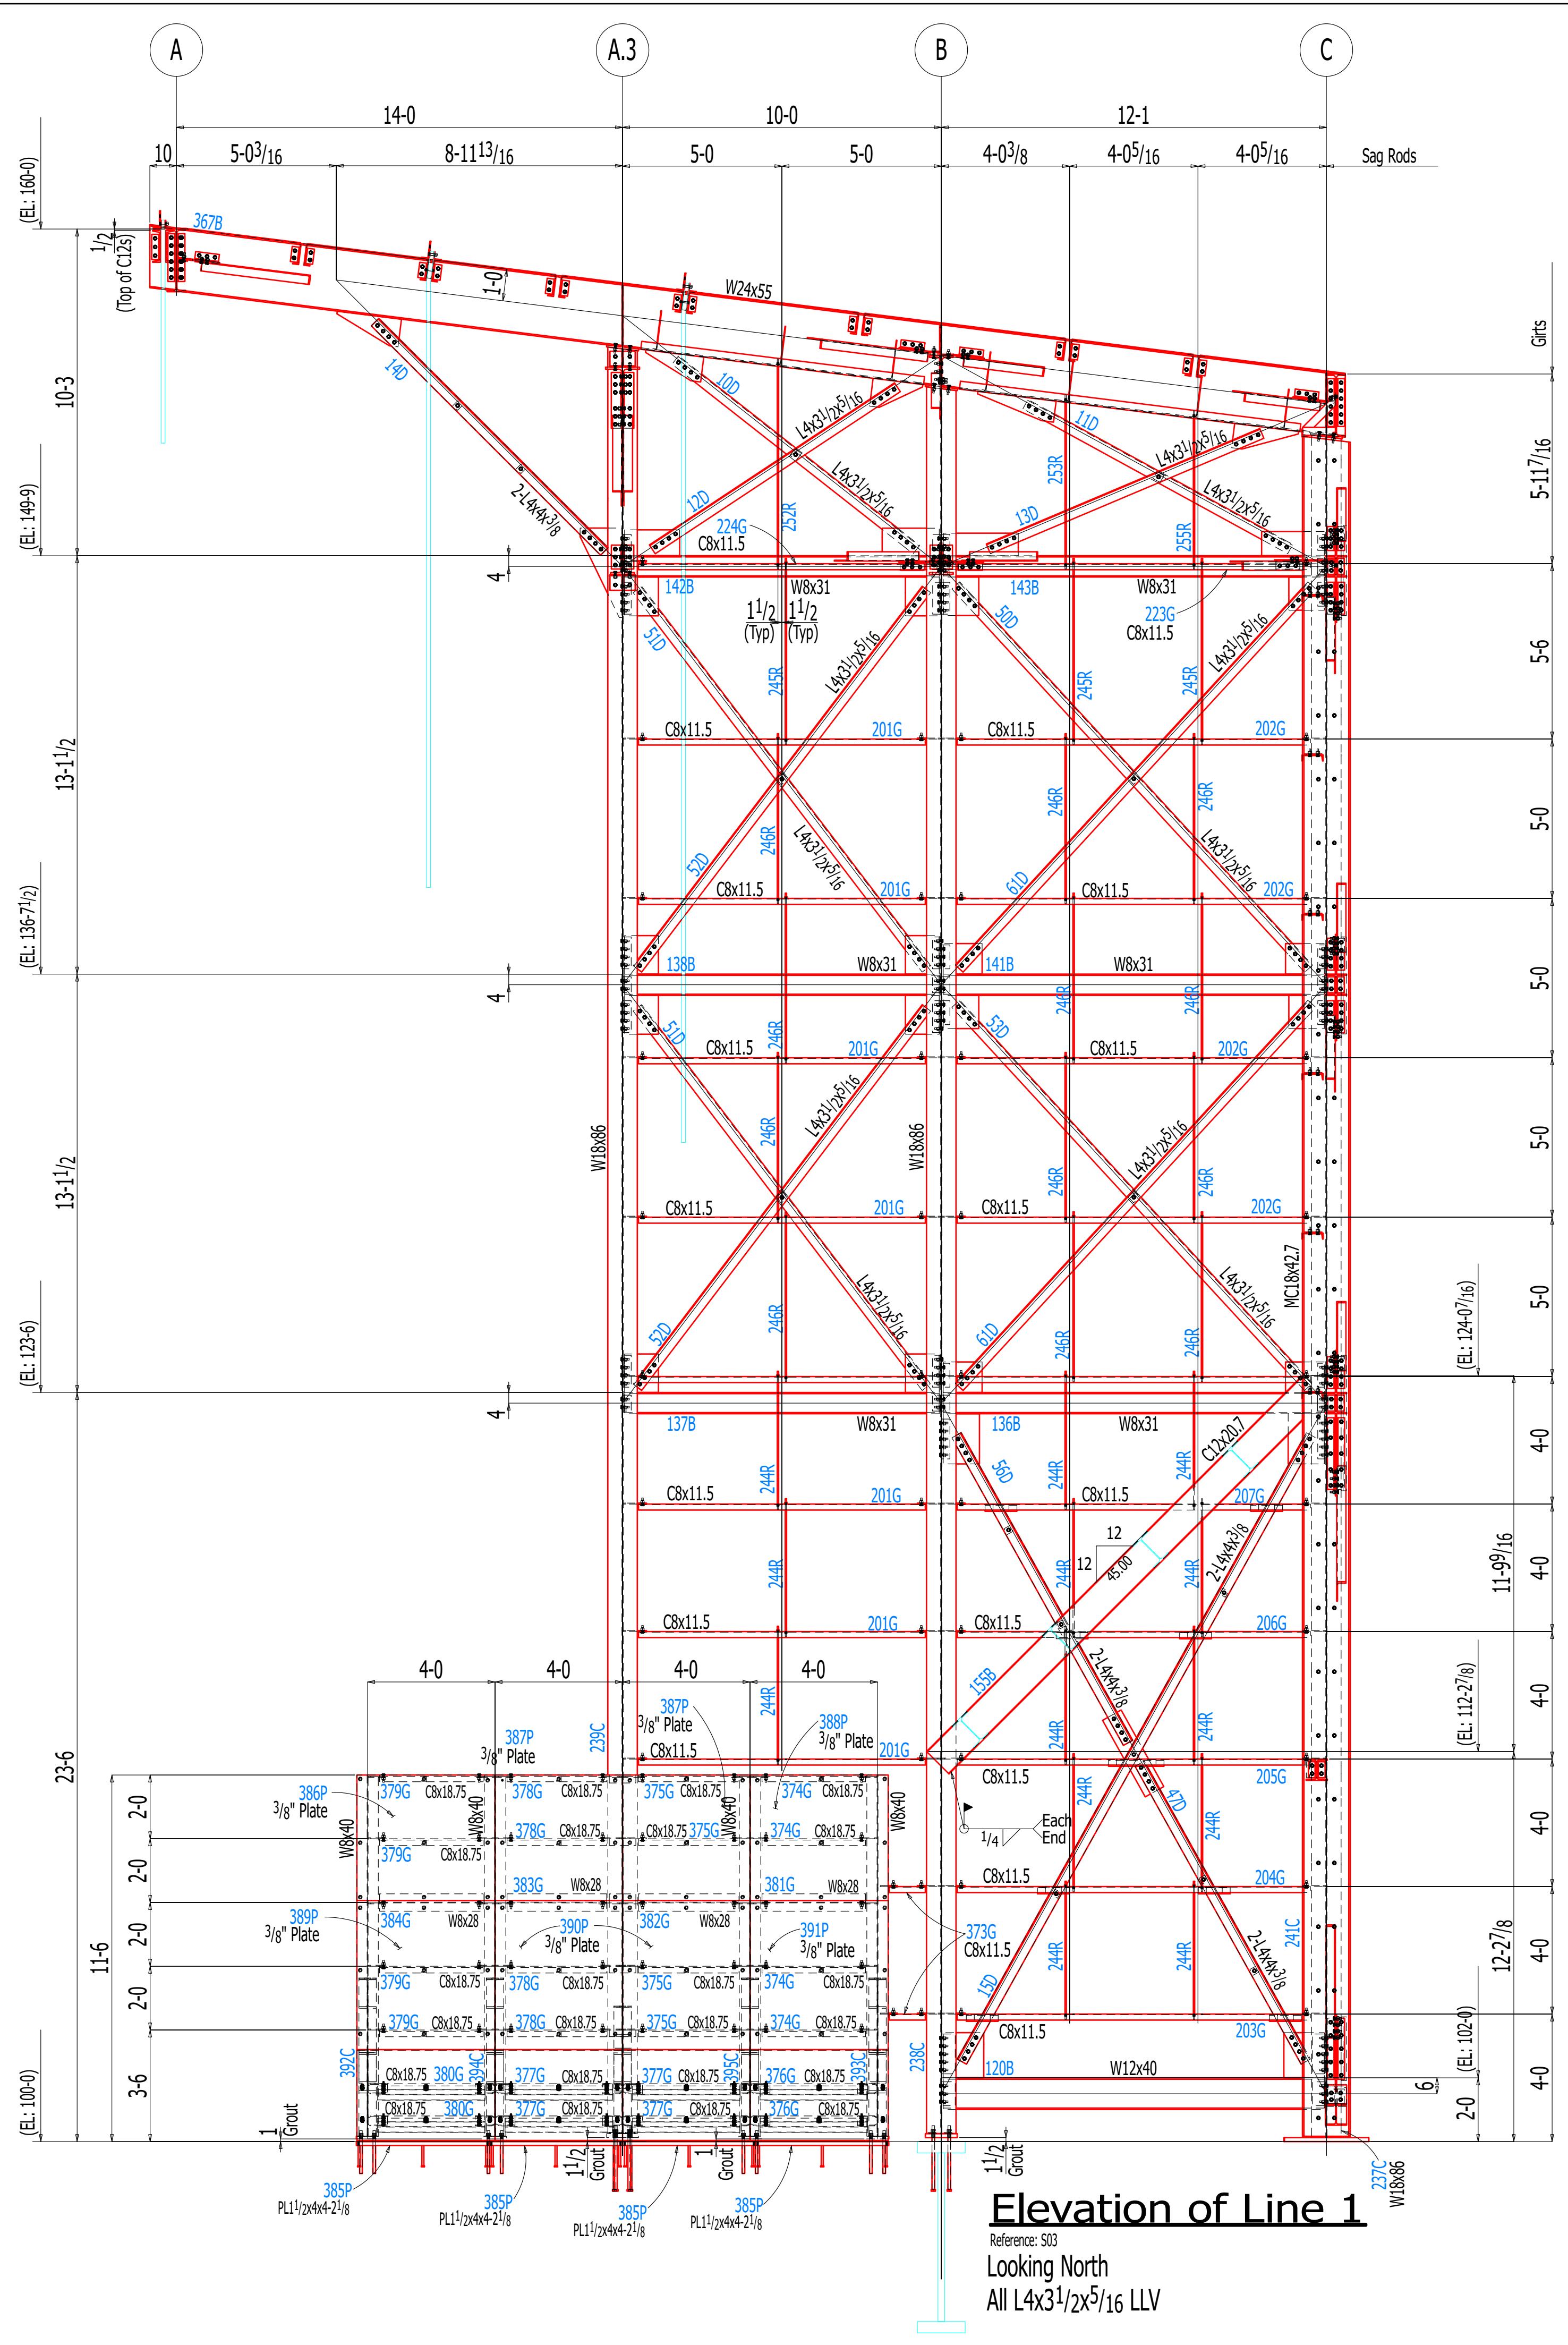



Elevation of Line

Reference: S03


Looking North

All 14x31/2x5/1c UV

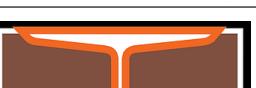0	For Field Use	May 22 2025	KR
B	Added Push Wall	Apr 2 2025	CR
A	For Approval	Feb 28 2025	CR
REV	DESCRIPTION	DATE	BY
FABRICATOR	DETAILER	DATE	BY
	PEPPER TANK & CONTRACTING	Nxt Gen Steel Detailing, LLC <i>Structural & Miscellaneous</i> PO Box 846 Basin, Wyoming 82410 307-272-5418 or 307-272-7031	DRAWN: 02-12-25 CR
001 W. Yellowstone Hwy, Casper WY 82602 - (307) 234-3533 - www.peppertank.com			CHKD: 05 22 25 NG
JOB NAME:	NARM - Stilling Shed Truck Dump (Circuit One)	HOLES:	13/16Ø UNO
LOCATION:	North Antelope Rochelle Mine - Gillette, Wy.	BOLTS:	3/4Ø A325N UNO
CONTRACTOR:	Hladky Construction	WELDS:	E70XX
SHEET DESCRIPTION:	JOB NUMBER:	SHEET NUMBER:	REV#
Elevation of Line 1 & 4	24-36N	E8	0

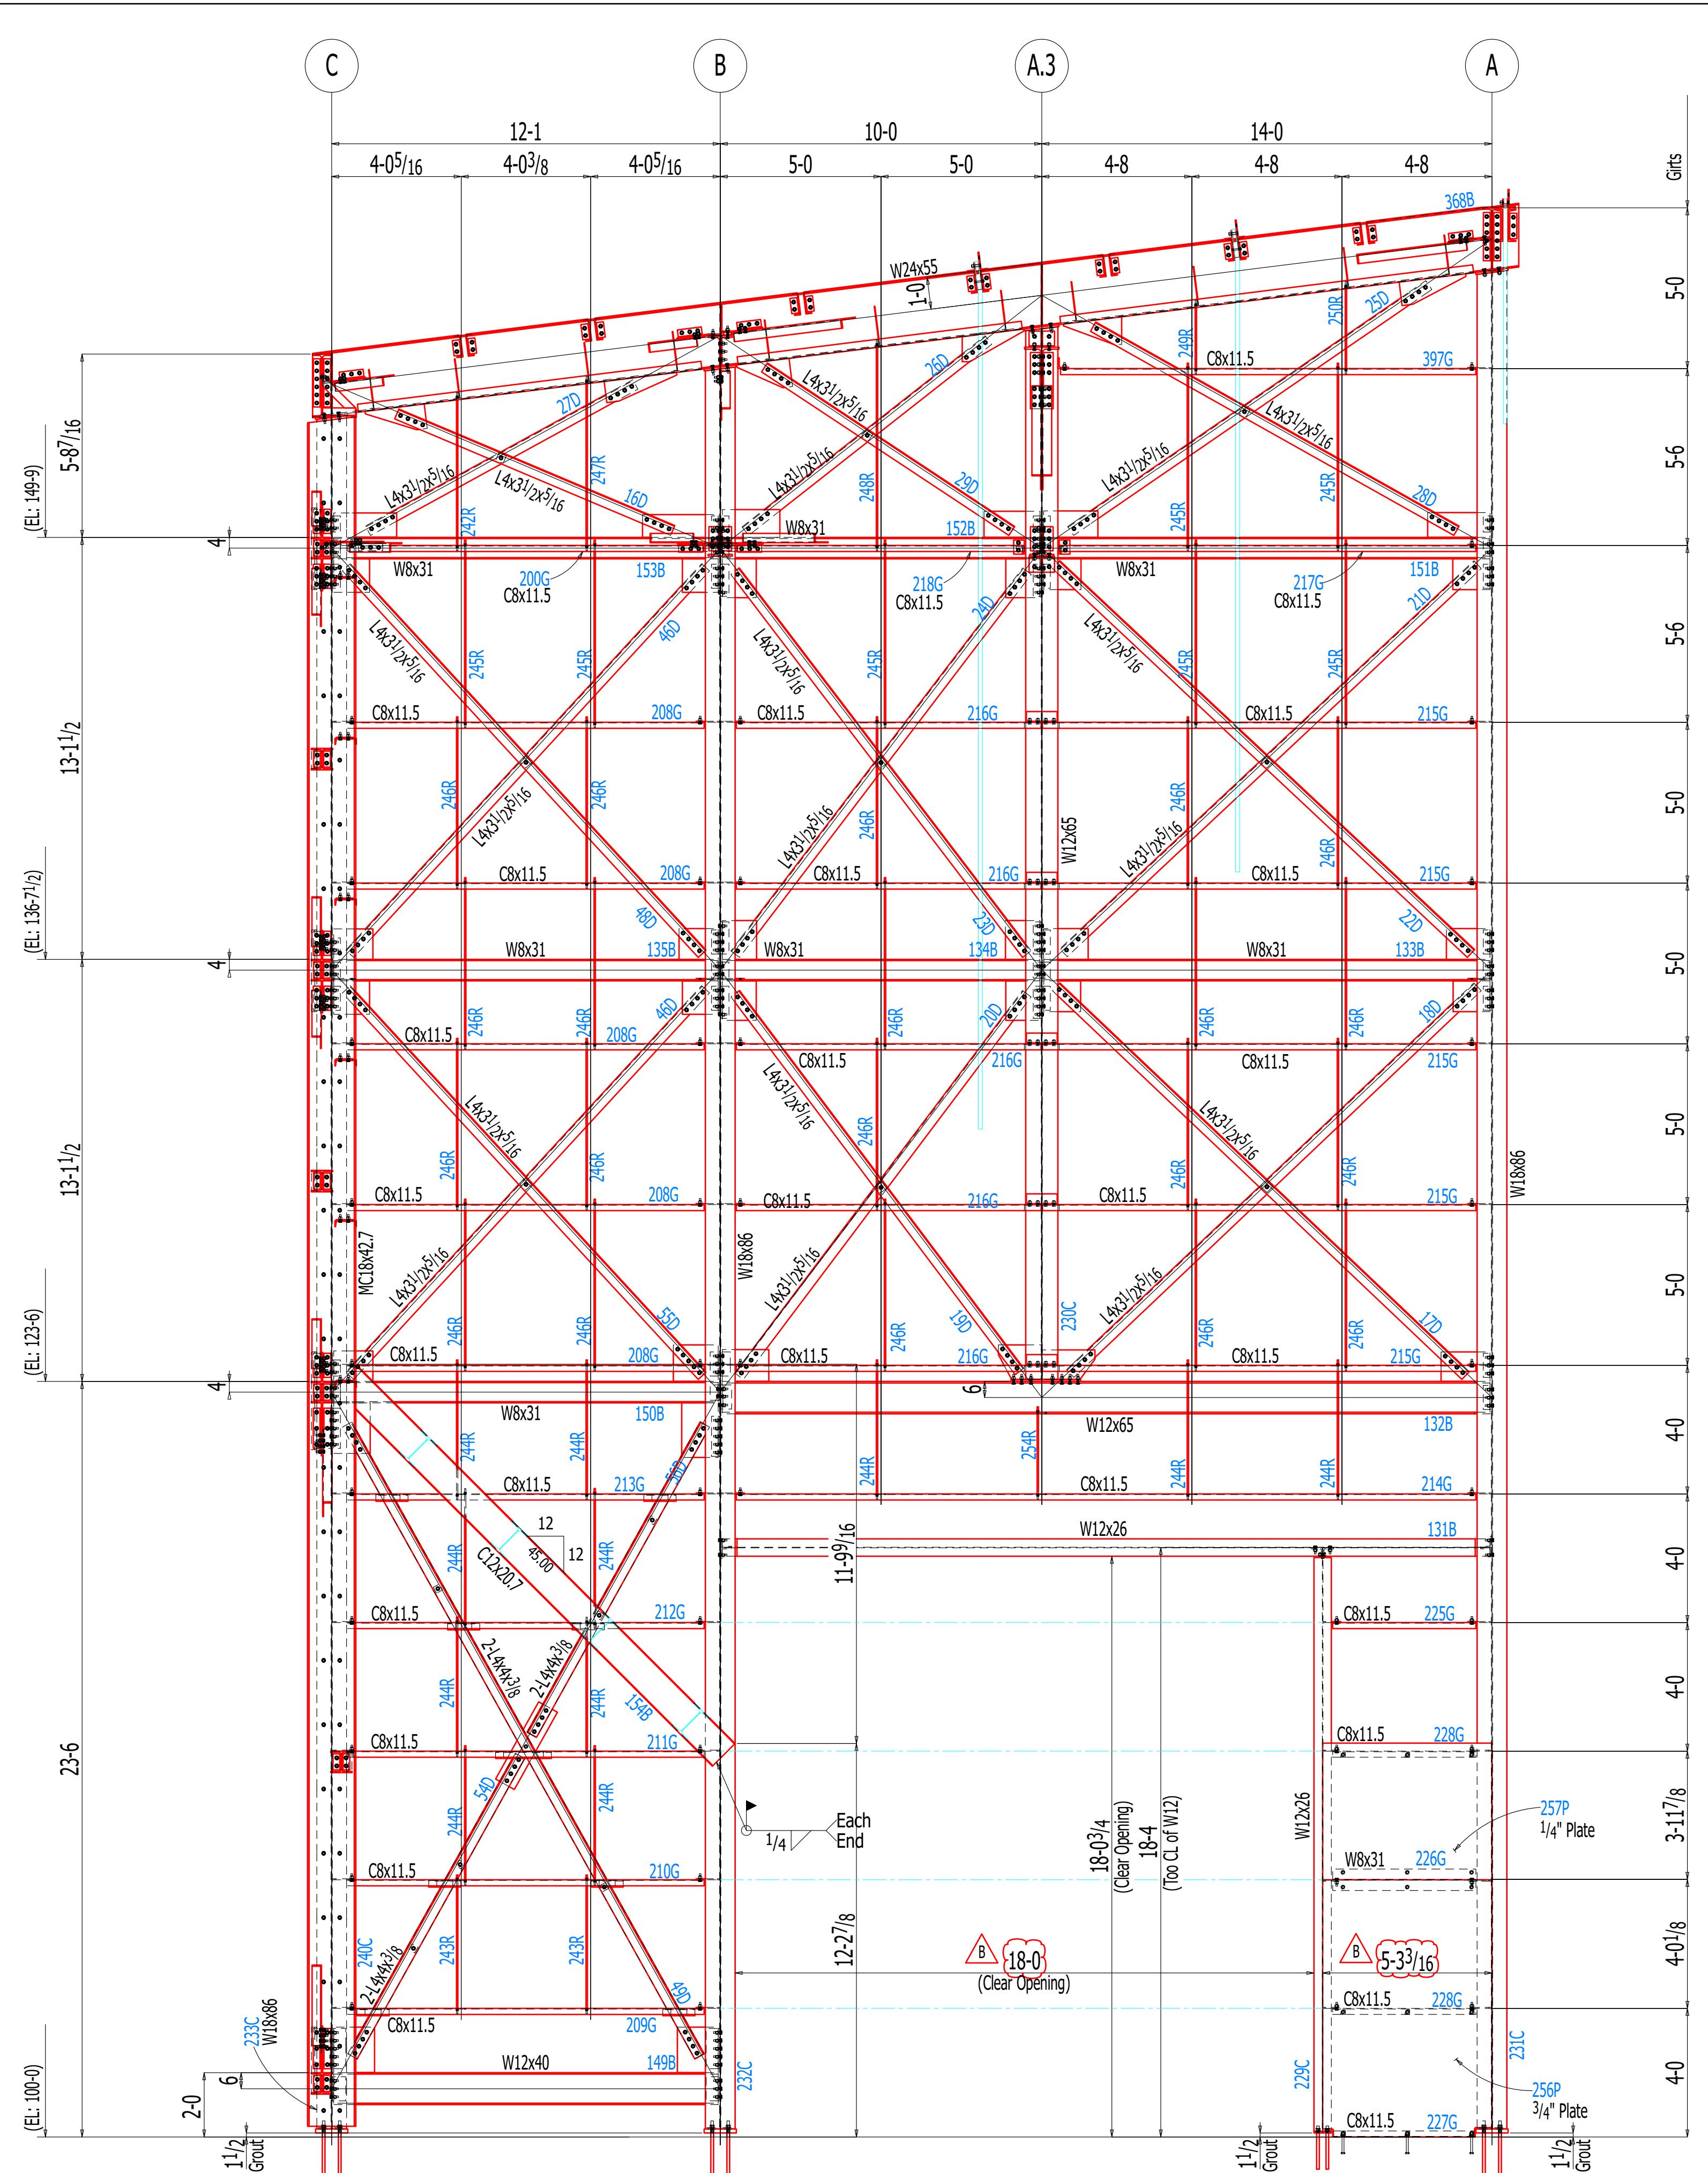

REV	DESCRIPTION	FABRICATOR	DETAILER	DATE	BY
0	For Field Use			May 22 2025	KR
B	Revised Overhead Door Opening			Apr 2 2025	CR
A	For Approval			Feb 28 2025	CR
REV	DATE	BY			
DRAWN:	02-12-25	CR			
CHKD:	02-12-25	NG			
HOLES:	13/16	UNO			
BOLTS:	3/4	A325N UNO			
WELDS:	E70XX				
CLEAN:					
PAINT:					
SHEET DESCRIPTION:	JOB NUMBER:	SHEET NUMBER:	REV#		
Elevation of Line 4	24-36N	E9	0		

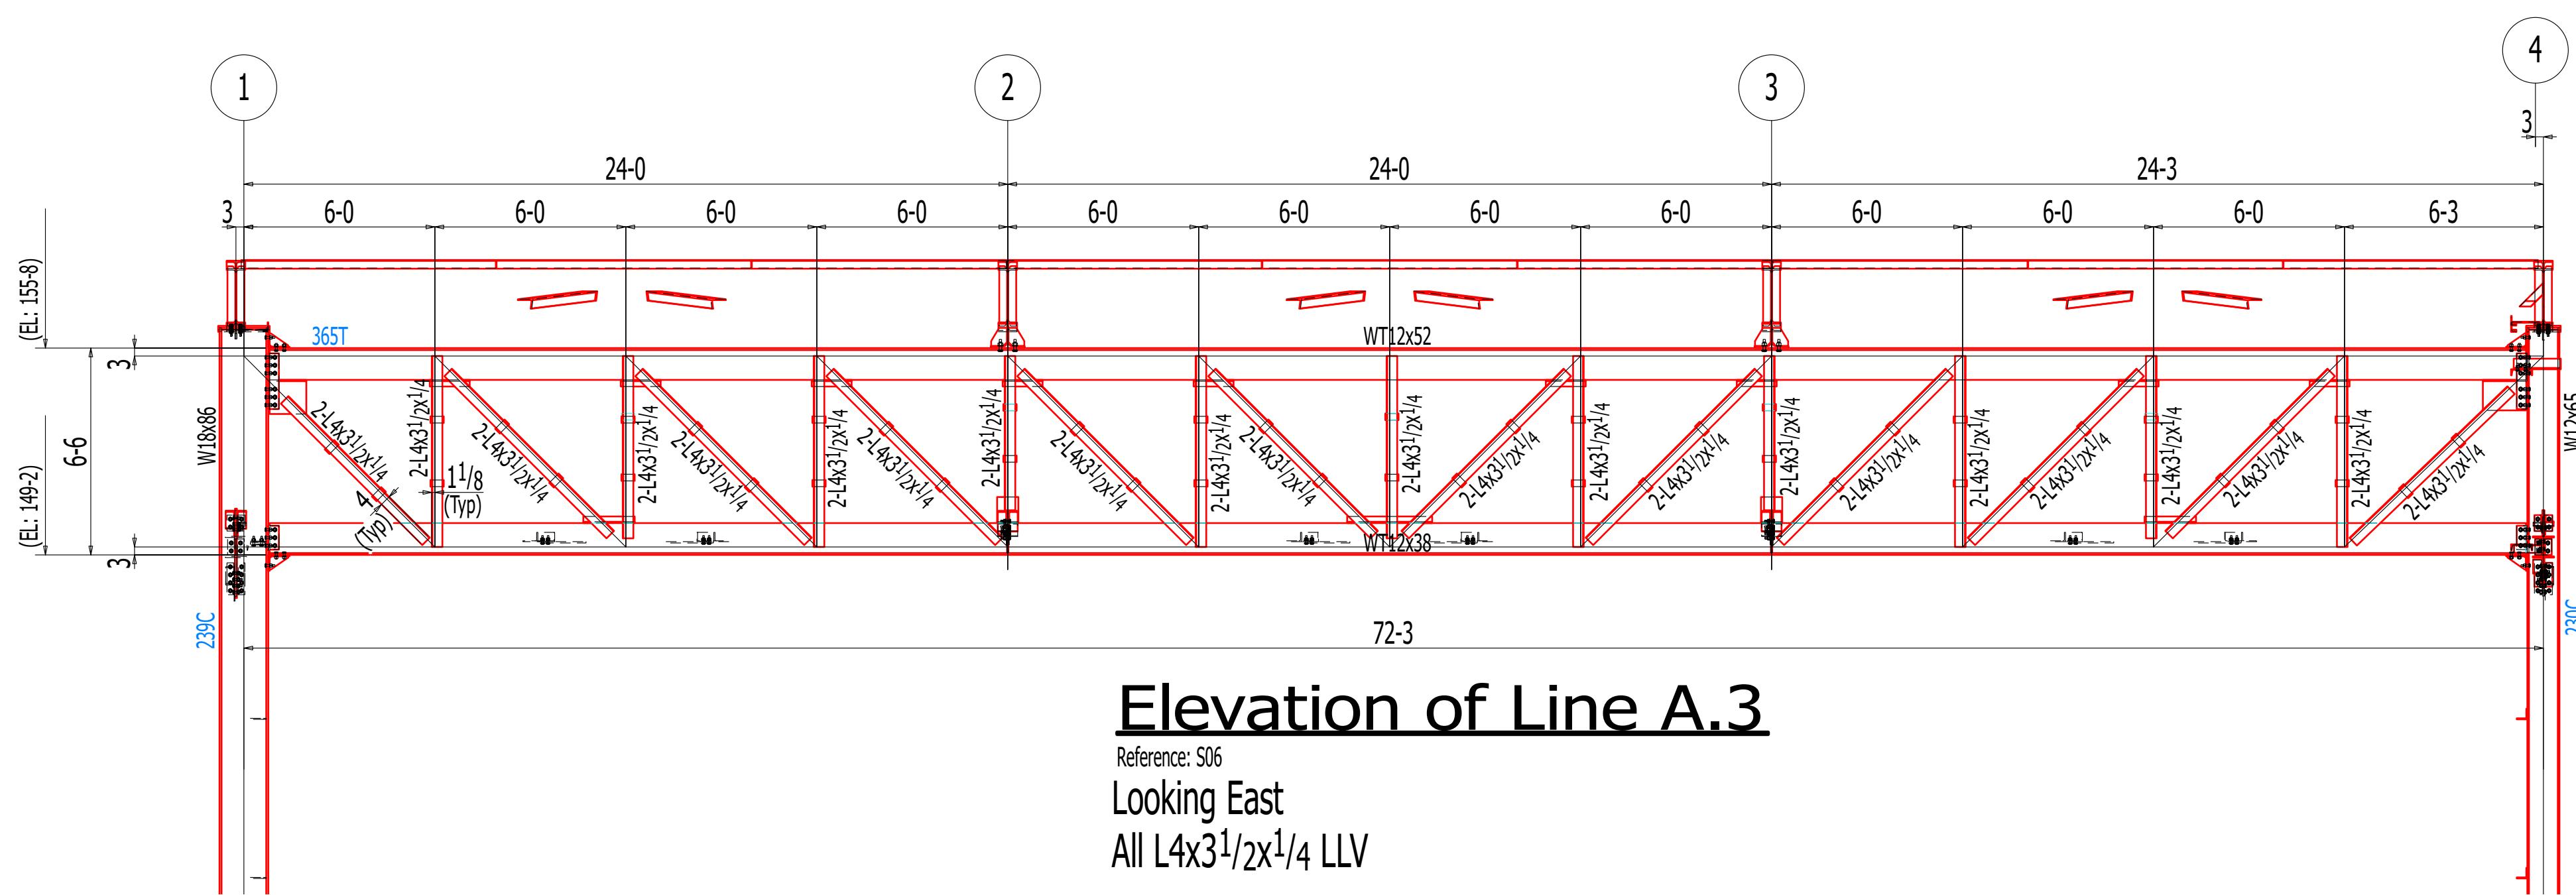


Elevation of Line A.3

Reference: S06

Looking East

All L4x3 1/2x1 1/4 LLV

PLOT SIZE: ARCH D [24x36]

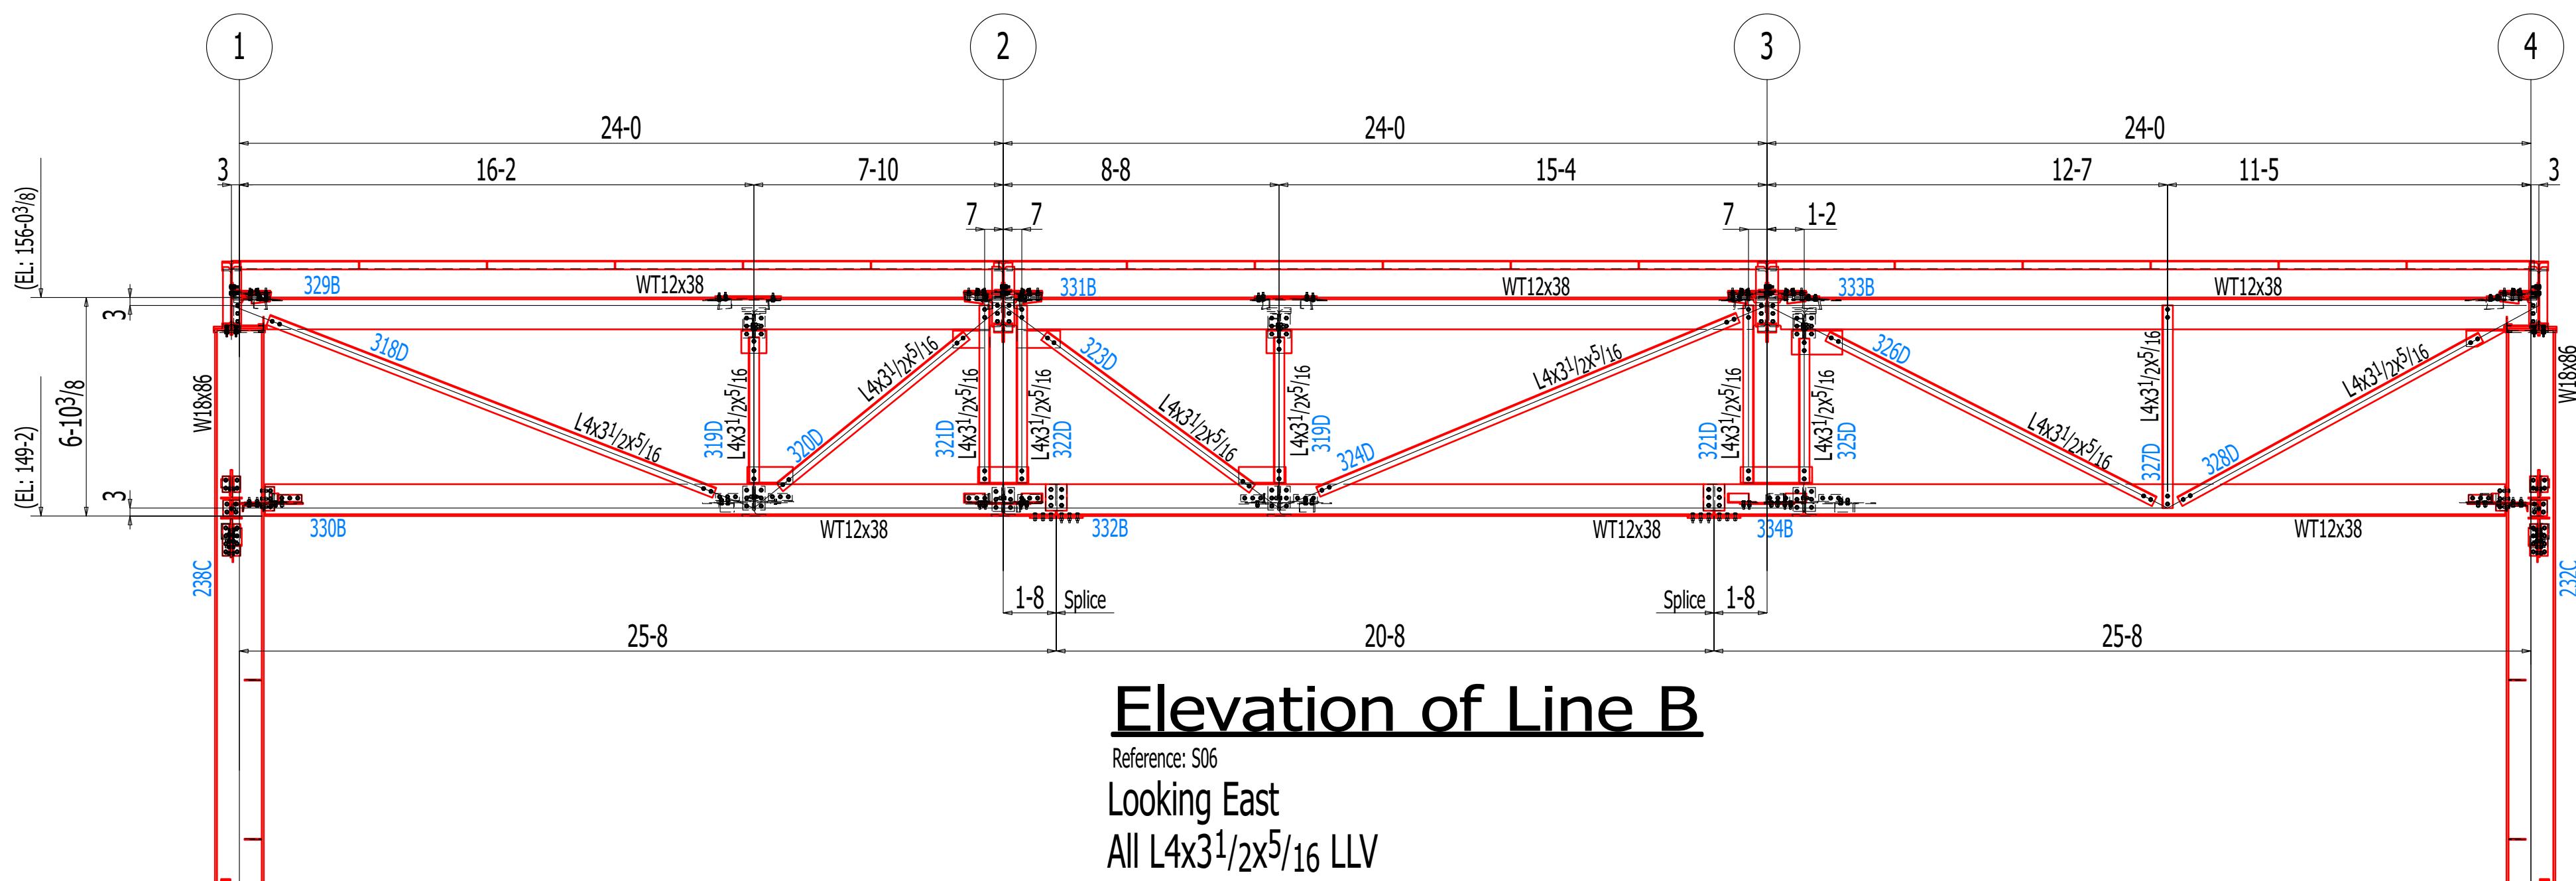


Elevation of Line B

Reference: S06

Looking East

All L4x3 1/2x5 1/16 LLV

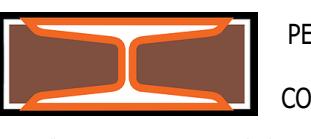0	For Field Use	May 22 2025	KR
A	For Approval	Apr 2 2025	CR
REV	DESCRIPTION	DATE	BY
	FABRICATOR	DETAILER	DATE BY
		Nxt Gen Steel Detailing, LLC Structural & General Contractors 1801 W. Yellowstone Hwy, Casper WY 82602 • (307) 234-3533 • www.peppertank.com	DRAWN: (02-12-25) CR
	PEPPER TANK & CONTRACTING		CHKD: 05 22 25 NG
			HOLES: 13/16Ø UNO
JOB NAME:	NARM - Stilling Shed Truck Dump (Circuit One)	BOLTS:	3/4" A325N UNO
LOCATION:	North Antelope Rochelle Mine - Gillette, Wyo.	WELDS:	E70XX
CONTRACTOR:	Hladky Construction	CLEAN:	
SHEET DESCRIPTION:	JOB NUMBER:	SHEET NUMBER:	REV#
Elevation of Line A.3, & B	24-36N	E10	0

PLOT DATE: May 22 2025